




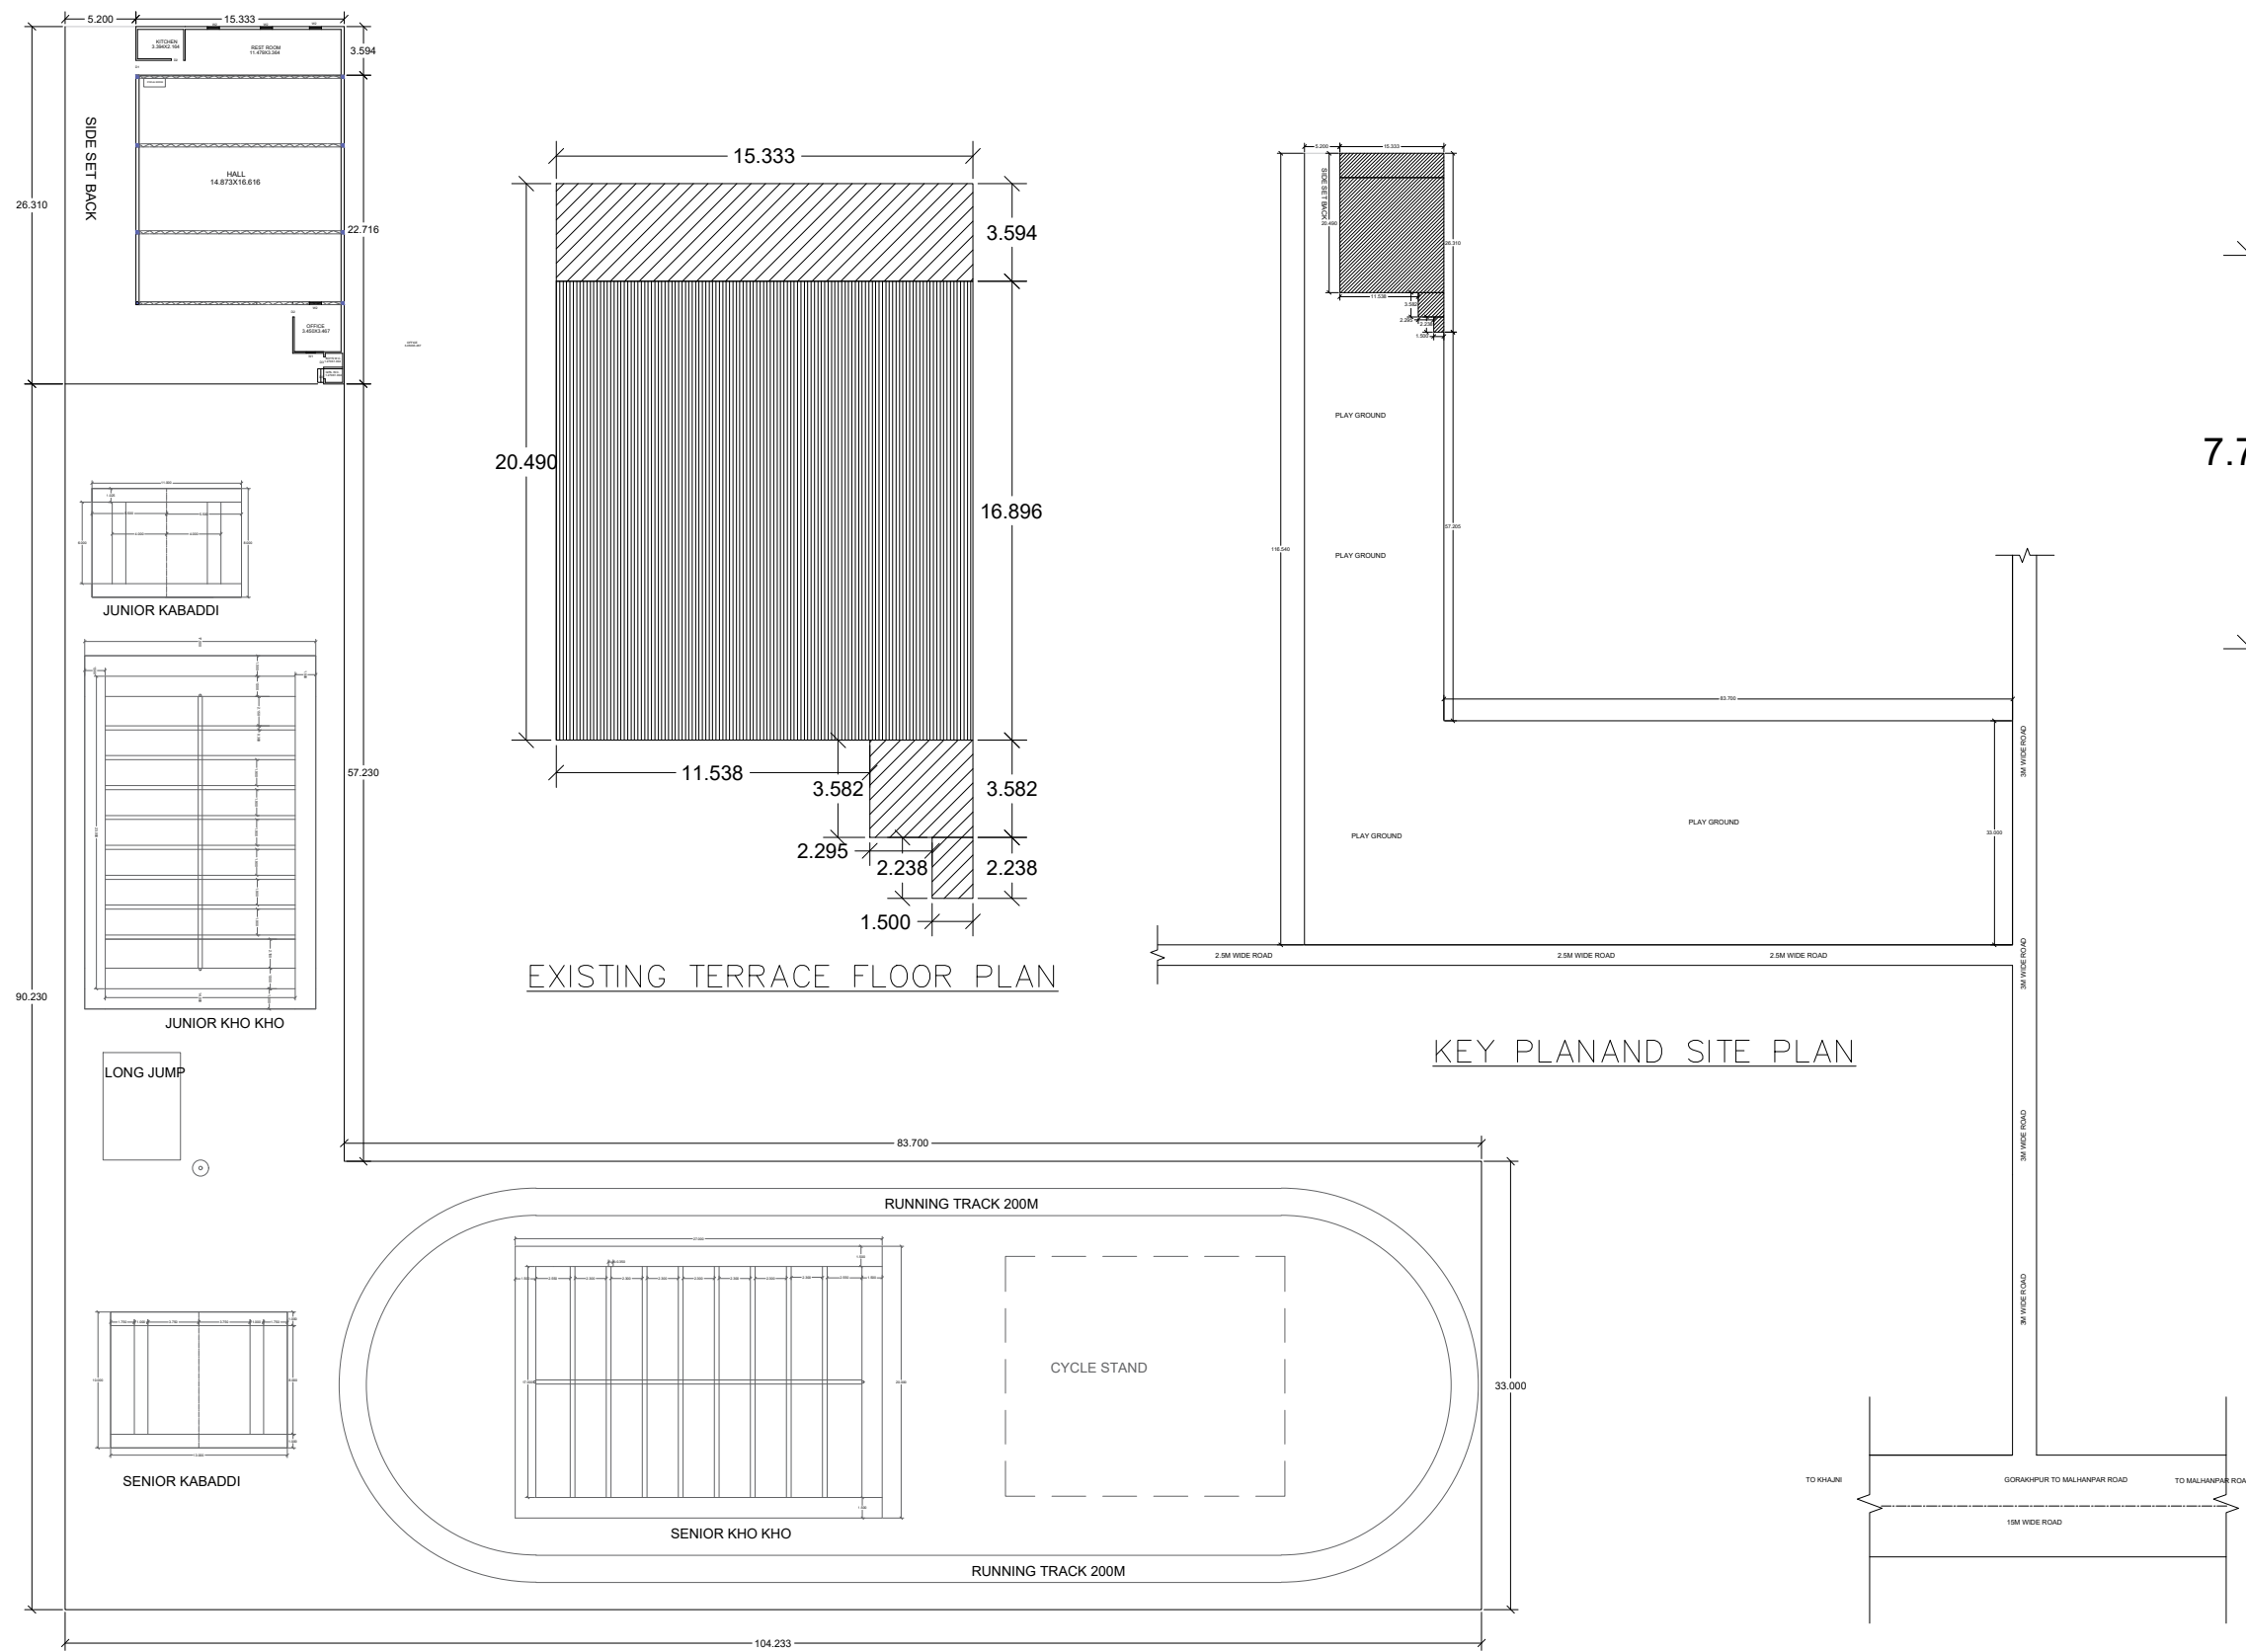


EXISTING GROUND FLOOR PLAN

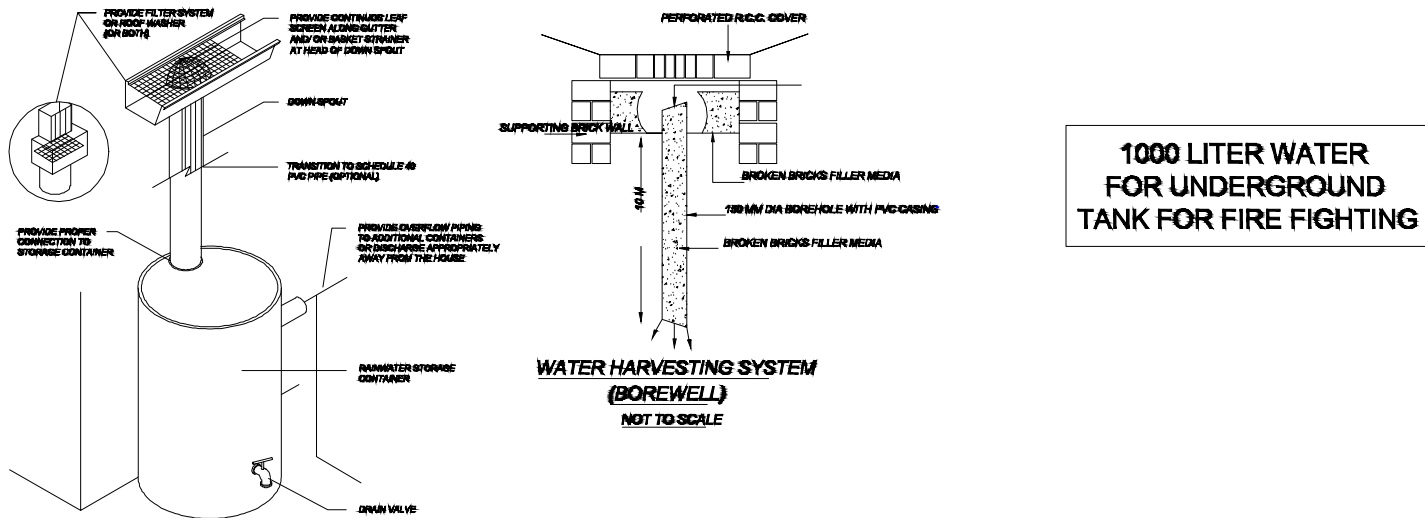


RAIN WATER HARVESTING

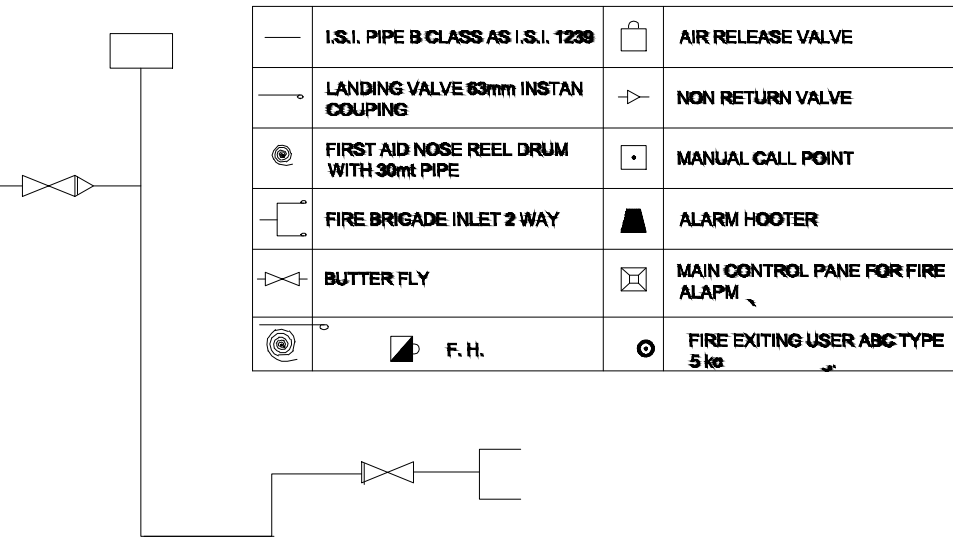


FIRE FIGHTING CHART

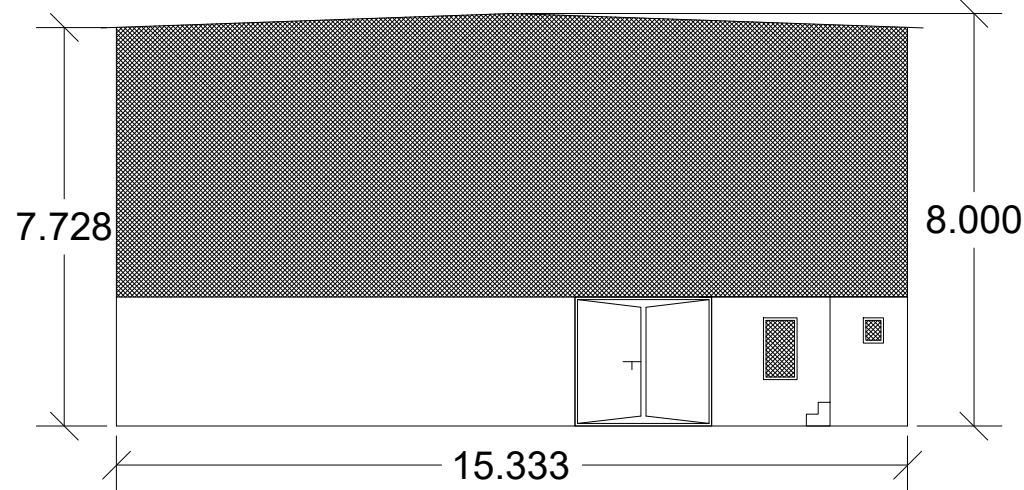

FRONT ELEVATION

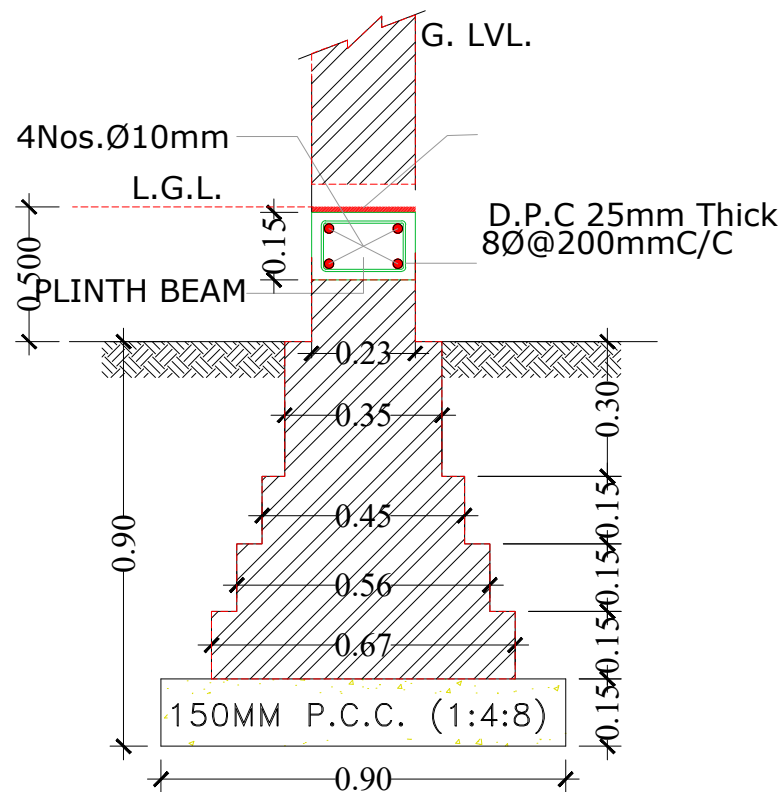

FOUNDATION

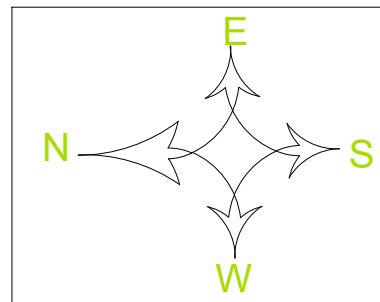

LEGENED

	FIRE EXTINGUISHER
	SMOKE DIRECTOR
	SIDE WALL TYPE SPRINKLER
	FLOW INDICATING
	BUTTERFLY VALVE
	FIRE HOUSE REEL BOX
	EXTERNAL FIRE HYDRANT
	TERRACE PUMP

SEAL

EXISTING MAHARANA PRATAP SPORTS ACADEMY(OPERATED ORGANIZATION MAHARANA PRATAP WELFARE ASSOCIATION) OF G.F. PLAN OF AT. - VILL+POST-MALHANPAR, TEH-KLHAJNI GORAKHPUR, PIN CODE-273403 UTTAR PRADESH

BUILDING HEIGHT =8M

AREA DETAILS

SL.	PARTICULAR	SQ.MT.
1.	TOTAL PLOT AREA	5155.016
2.	COVERED AREA OF G.F.	331.124
3.	SIDE SET BACK	5.20M WIDE
4.	JUNIOR KABADDI PLAY GROUND	88.00
5.	JUNIOR KHO KHO PLAY GROUND	442.00
6.	SENOIR KABADDI PLAY GROUND	130.00
7.	SENOIR KHO KHO PLAY GROUND	540.00
8.	RUNNING TRACK	200M
9.	TOTAL COVERED AREA OF BUILDING	331.124
	GROUND COVERAGE	15.56%

ROAD WIDTH =3 M

SCHEDULE OF OPENING

SL.	PARTICULAR	SYMBOL	WIDTH	HEIGHT
1.	DOOR	D1	1.20	2.10
2.	DOOR	D2	0.90	2.10
3.	DOOR	D3	0.75	2.10
4.	WINDOW	W	1.00	1.20
5.	WINDOW	W1	0.90	1.20
6.	VENTILATER	V	0.60	0.45
7.	VENTILATER	V1	0.45	0.30

STAIR DETAILS
RISER = 0.230M
TREAD = 0.230M
WIDTH = 1.000M

SCALE
N.T.S

ENGINEER'S SIG.

OWNER'S SIG.

Dr. Mahendra Singh
(Civil Engineer)
Awes Bandhu
Reg. No.-AM1951974/1012020
Sufiyan